


Úprava priechok

LEGENDA MIESTNOSTÍ		
ČÍSLO MIEST.	NÁZOV MIESTNOSTI	PLOCHA
1.	Predsieň	9,84m²
2.	Kúpeľňa	5,62m²
3.	Pracovňa	14,82
4.	Spálňa	19,67
5.	Obývačka	20,34
6.	Kuchyňa	9,38m²
Celková plocha spolu		79,67

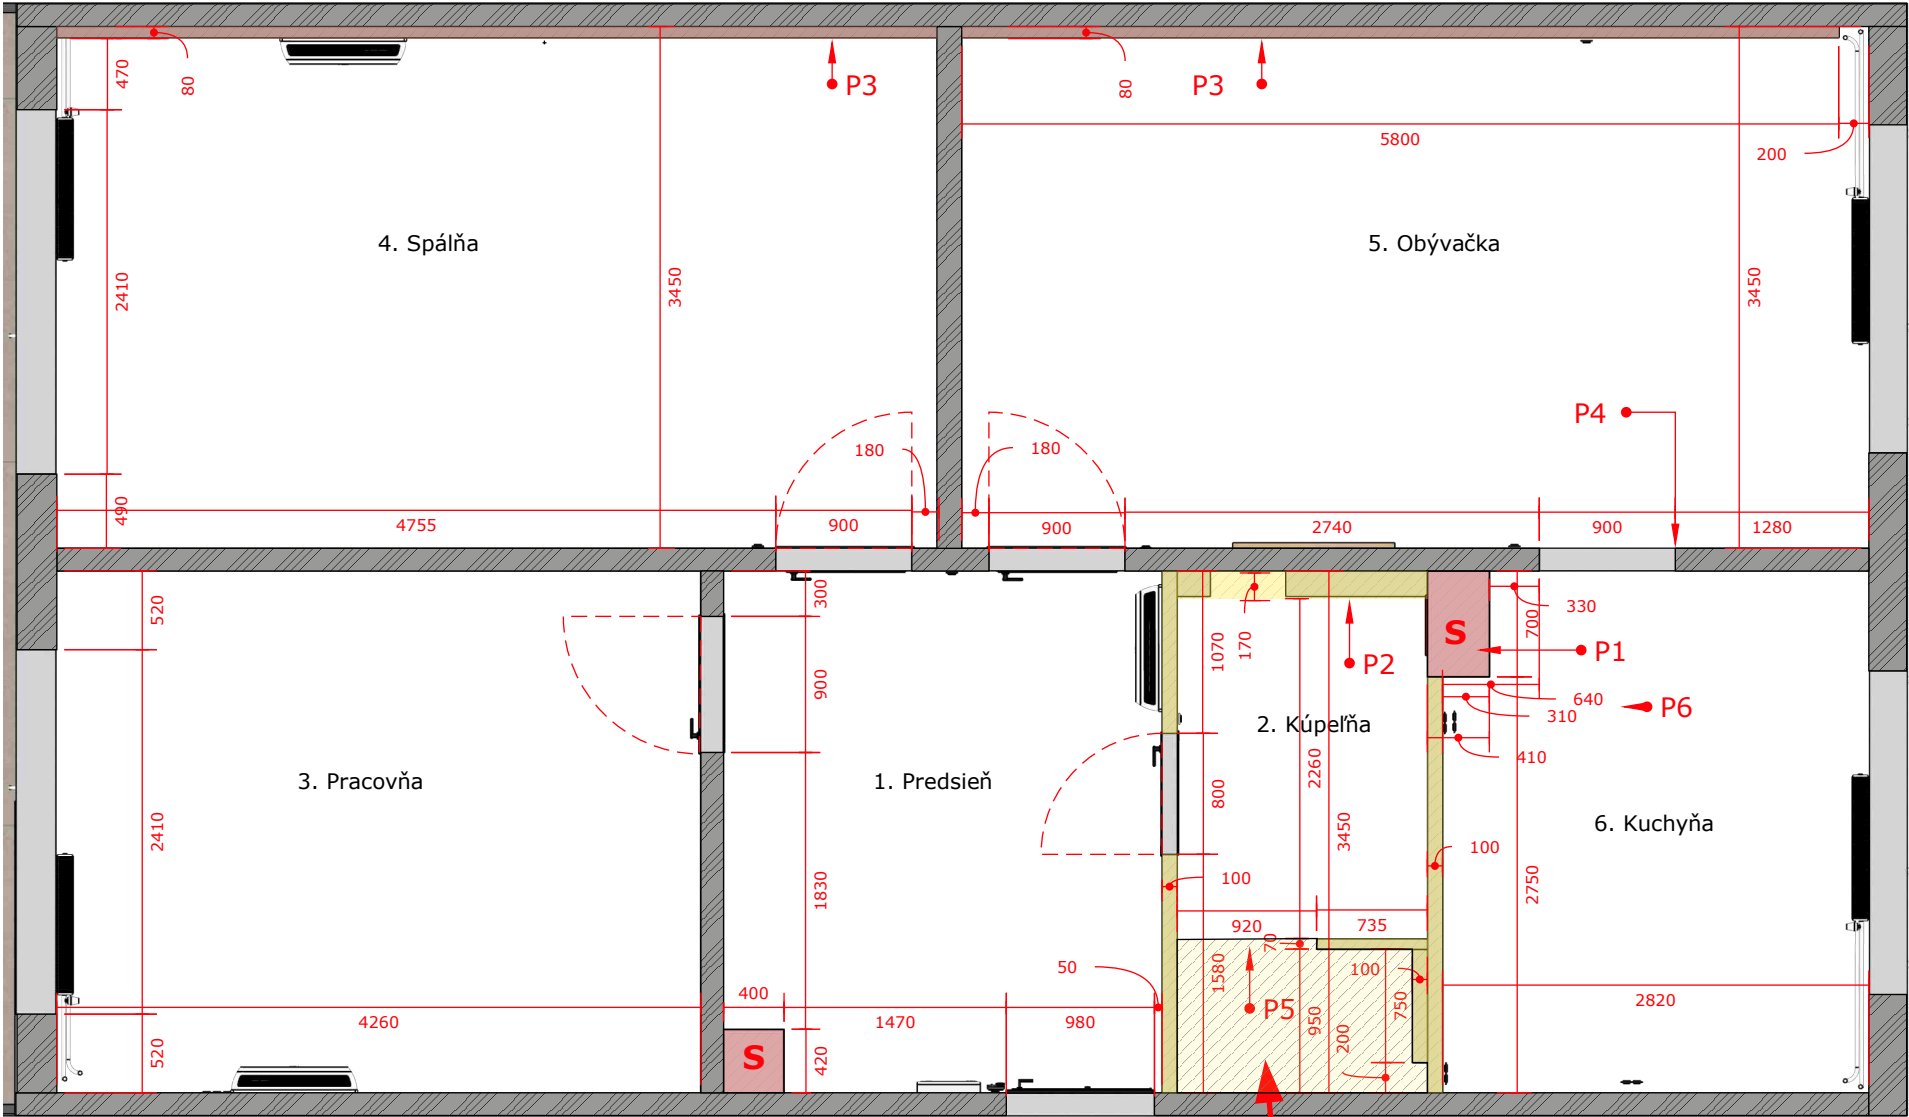

Poznámky

- P1** - Po kapotáži stúpačky je potrebné zmerať finálne rozmery a poslať ich na kontrolu. Od stúpačky závisia rozmery kuchynskej linky!
- P2** - Pre umiestnenie WC(Geberit) je potrebné vytvoriť primúrovku 170mm,1200v. Ak by bolo potrebné pre koleno zväčšiť hĺbku, je potrebné zamerať finálny rozmer a poslať mi ho.
- P3** - V miestnostiach 4 a 5 je potrebné vytvoriť SDK akustickú predstenu
- P4** - Novovytvorený priechodzí otvor.
- P5** - Priechodzí otvor do sprchy musí mať 920mm (už s obkladom) tak aby sa doň dali umiestniť krídlové dvere v štandardnom rozmere 900mm.
- P6** - Finálny rozmer medzi stenou kúpeľne a dverným otvorom nesmie byť menší ako 640mm, úpravu P4 treba spraviť až po kapotáži stúpačky kvôli kontrole rozmerov!

Legenda


- Nenosné priečky
- Nenosné priečky nové
- Nosné priečky
- S

Stúpačka
- Akustická SDK predstena

P7 - V priestore sprchy je potrebné vytvoriť pódium s výškou (?) s dostatočným spádom pre odvod vody formou zníženého žľabu APZ115 Marble Low - vzdialenosť žľabu od stúpačky 2200 mm (prípadne použiť APZ104 Flexible Low ak by nevychádzal spád)

Autor: Jakub Pevný	Jednotky	Mierka	Strana
27.07.2026	mm	1:50	1
Stavebné úpravy			



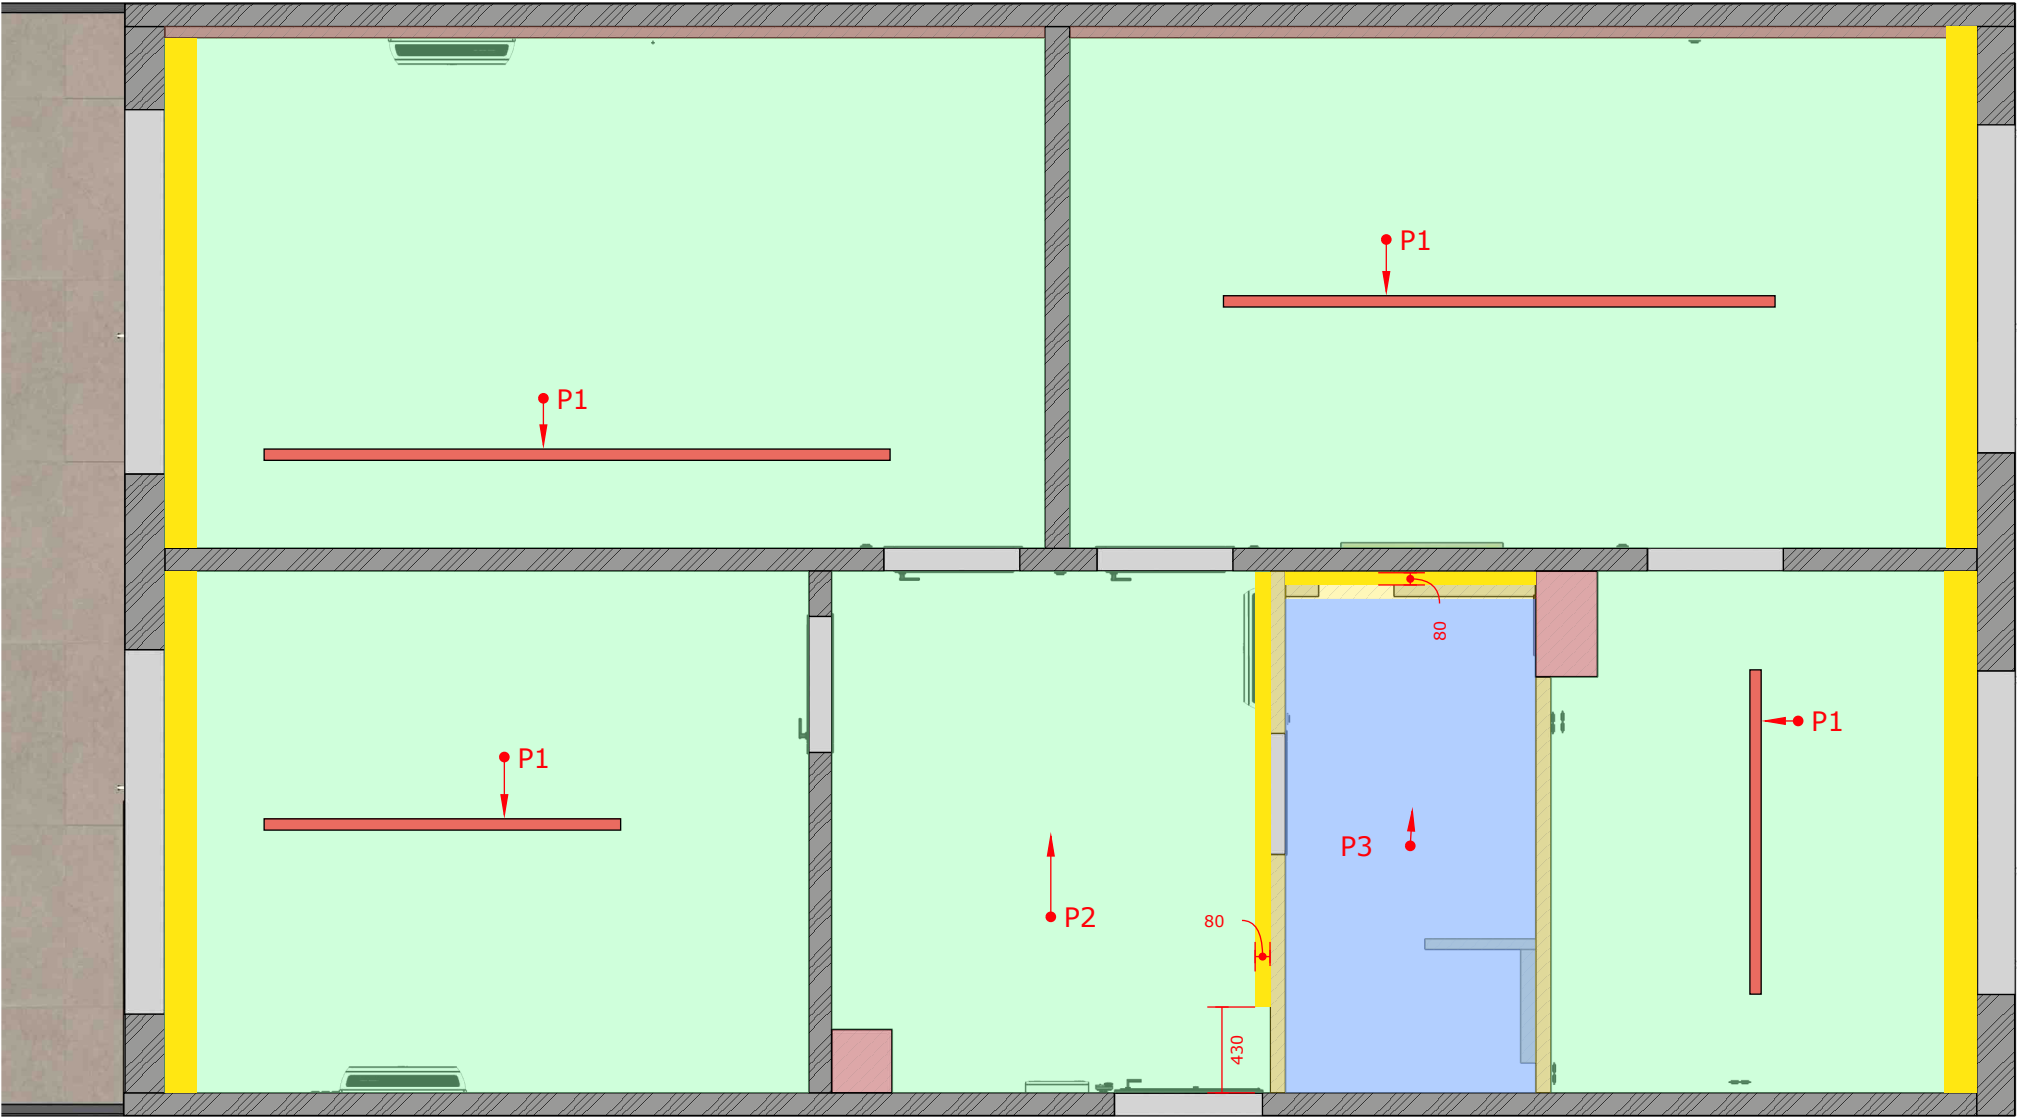


Poznámky

P1 - Ako hlavné stropné osvetlenie je plánovaný zapustený magnetický systém NANO - LVM od značky Nowodvorski

P2 - V predsieni bude stropné osvetlenie formou zapustených bodových svietidiel. (podrobnosti na strane Stropné osvetlenie)


Rampa pre LED osvetlenie závesov

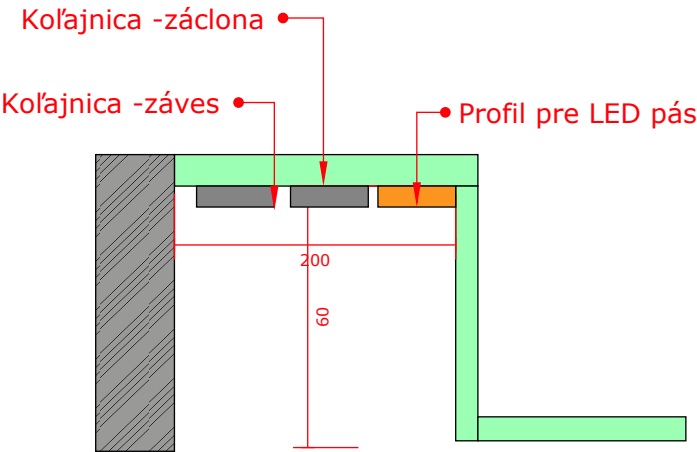

Legenda

- SDK - Suché prostredie - 73,93 m2
- SDK - Prostredie so zvýšenou vlhkosťou - 5,71m2
- Rampa pre LED osvetlenie

Autor: Jakub Pevný	Jednotky	Mierka	Strana
27.07.2026	mm	1:50	2

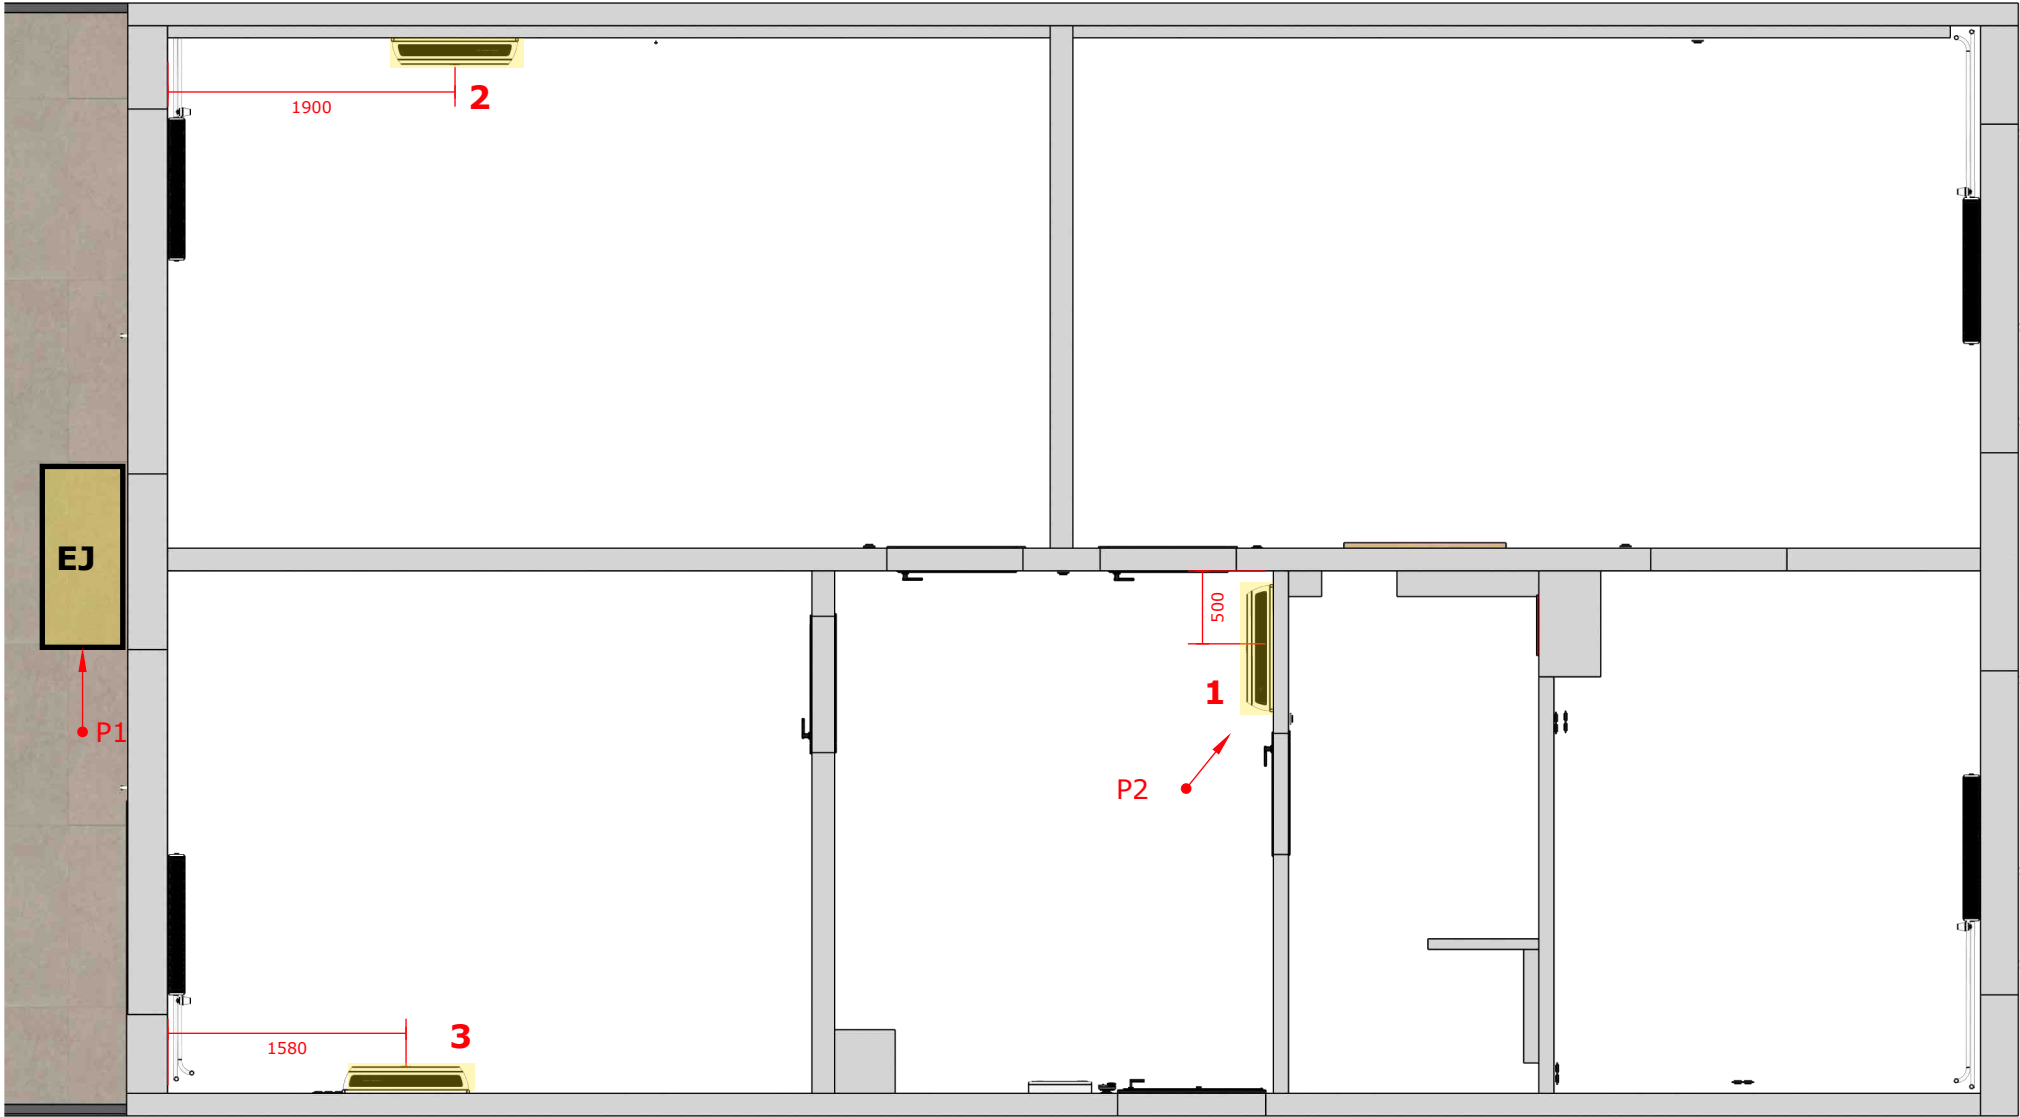

Poznámky


- P1** - Umiestnenie vonkajšej jednotky na balkóne, odvod kondenzu pre KJ 2 a 3 bude vedený na balkón.
- P2** - V projekte sa ráta s Triple-split klimatizáciou, odvod kondenzu pre KJ 1 bude vedený do odpoadu kúpeľne.

Legenda


 Vnútorne klimatizačné jednotky

Autor: Jakub Pevný	Jednotky	Mierka	Strana
27.07.2026	mm	1:50	3
Elektro inštalácie - 1.časť - Klimatizačné jednotky			



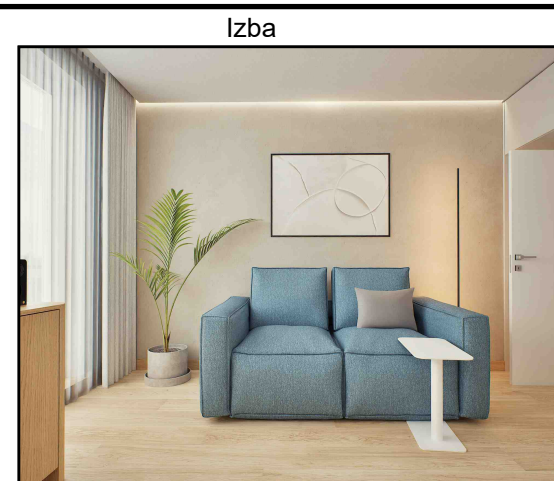

Elektroinštalácie Svietidlá

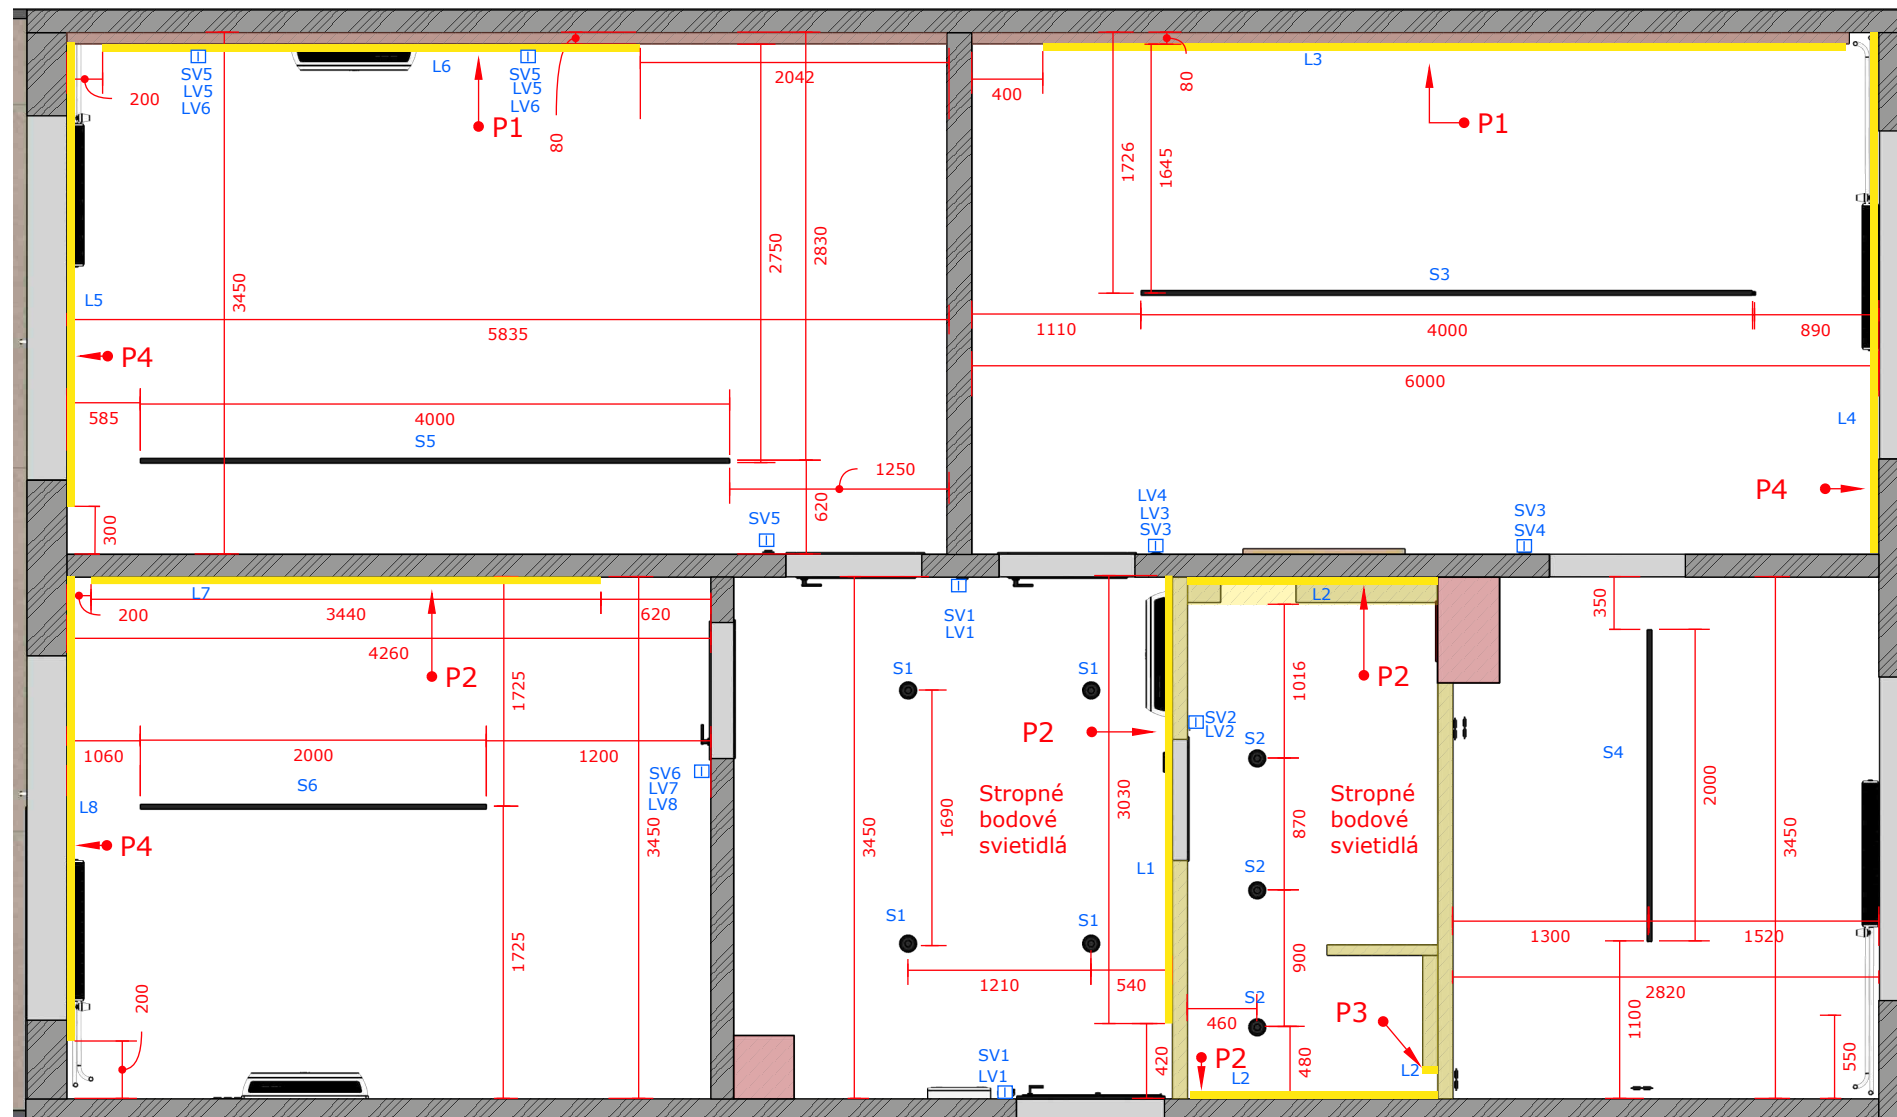

Poznámky

LED pásy sú deliteľné každých 5cm.

Umiestnenie napájania (trafo) pre LED svietidlá je na strane elektroinštalácií.

Pre LED svietidlá použiť dim + teplota - vypínač

Pre lepšie ovládanie odporúčam použiť pre LED svietidlá - SMART TUYA spínač (nutná wifi brána pri routery + prijímač pre každé LED svietidlo - možnosť nastavovať svetelné scény) - NUTNÉ POUŽIŤ HLBSIE KRABIČKY

<https://www.123led.sk/smart-spinac-tuya-pre-led-svietidla-230v/>

Alternatíva pre napájanie LED - inštalovať väčšiu rozvodnú skriňu a umiestniť priemyselné trať + smart drivery (na spôsob Loxone)



P1 - SDK (alebo styrodur) panel s LED pásom zo spodnej a vrchnej hrany - umiestnený 4cm pod hranou.

P2 - LED Rampa pre nasvietenie obkladov (zo strany SDK prvkov - hĺbka 80mm)

P3 - Nasvietenie niky v sprche - IP67

P4 - LED Rampa pre nasvietenie závesov (zo strany SDK prvkov).

Nowodvorski
NANO - LVM RECESSED TRACK 2M 11731

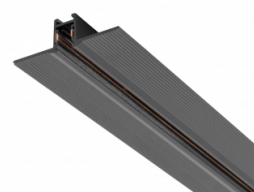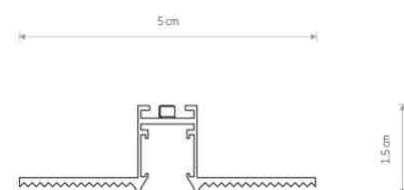

Nowodvorski
CUP 10788



LED

CCT COB LED pásik 15W/m
24V bez krytia IP20

Výkon: 15W/m. Počet LED diód: 576/m.
Krytie: IP20. Svetivosť: 1400lm/m.
Teplota svetla: 2700K - 6500K.
Vstupné napätie: DC 24V.



LED do kúpeľne

COB LED pásik 10W/m
24V vodeodolný IP67

Výkon: 10W/m. Počet LED diód: 480/m.
Krytie: IP67. Svetivosť: až 1040lm/m.
Teplota svetla: 3000K, 4500K, 6500K.
Vstupné napätie: DC 24V.



<https://nowodvorski.sk/svietidlo-nano---lvm-recessed-track-2m-11731>

<https://nowodvorski.sk/svietidlo-cup-10788>

Autor: Jakub Pevný

Jednotky

Mierka

Strana

27.07.2026


mm

1:50




4

Elektroinštalácie - Svetidlá



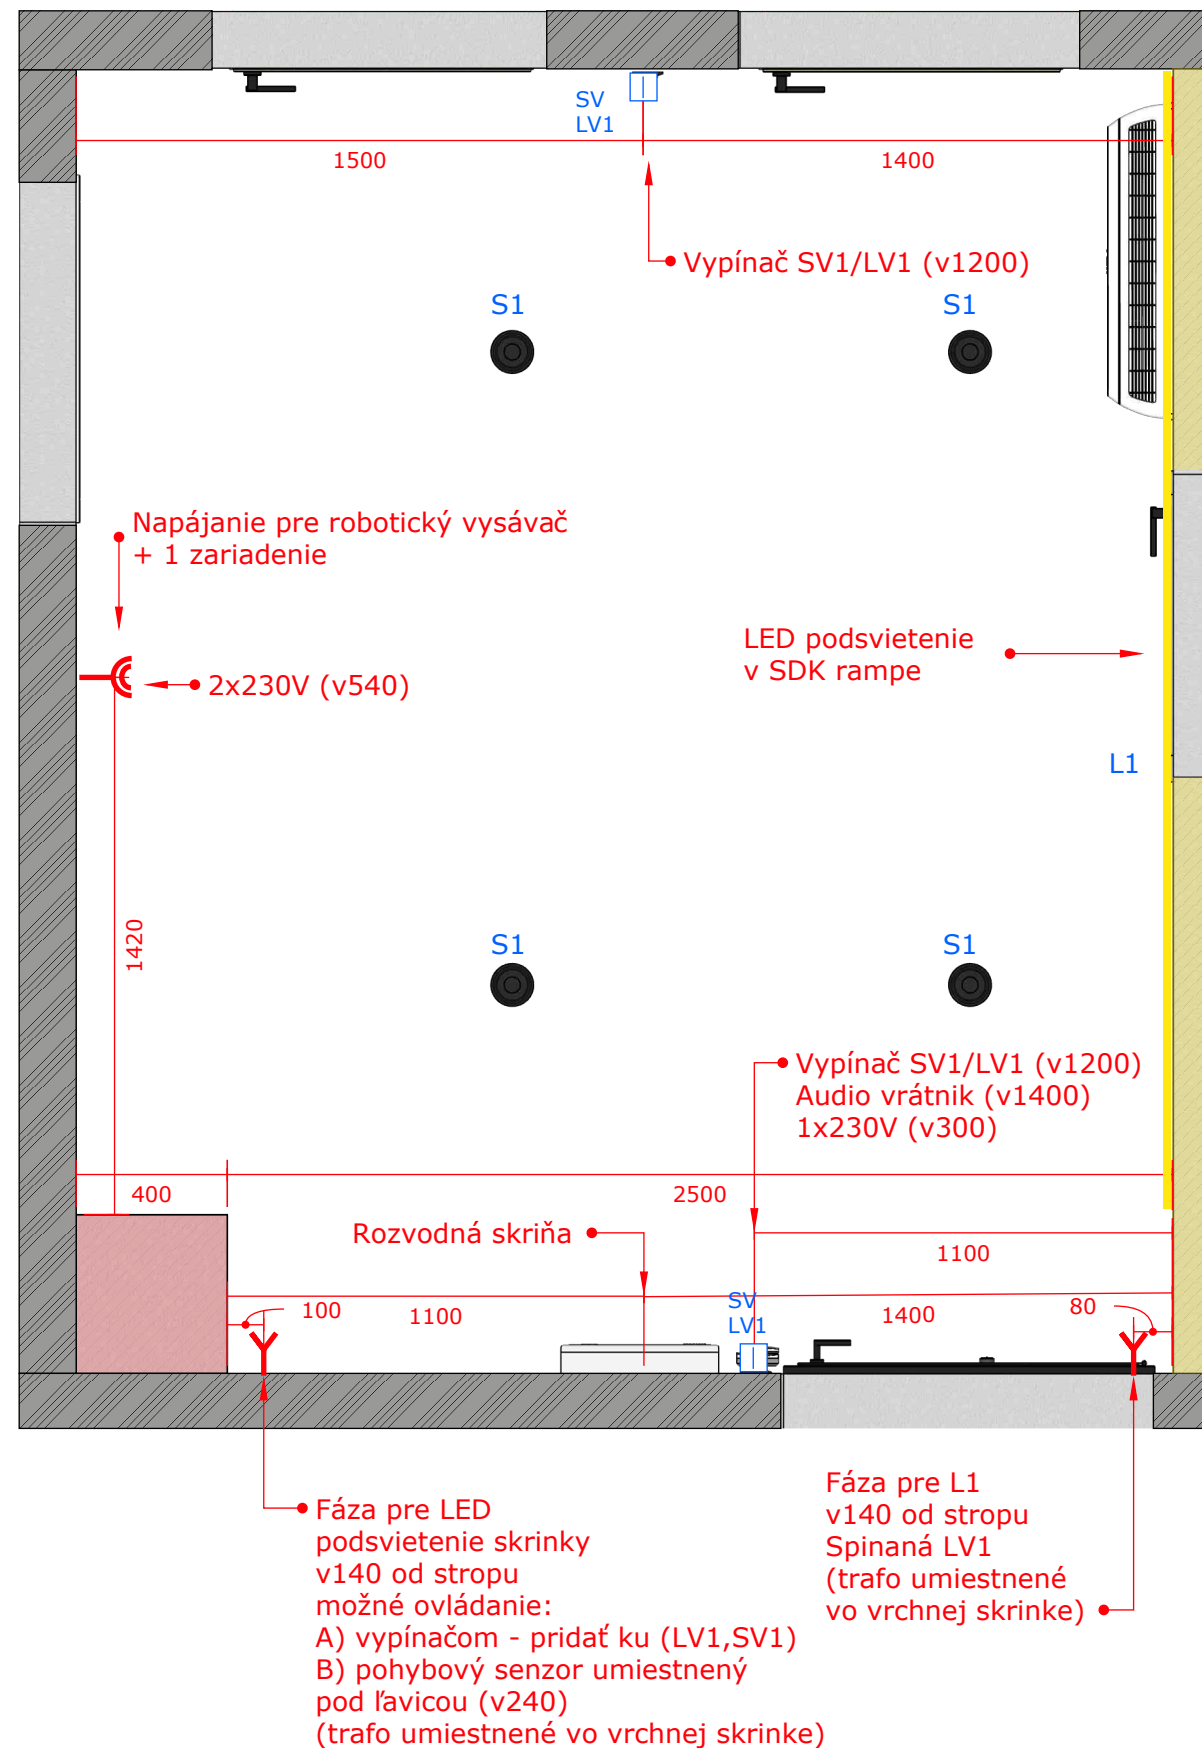

Vizualizácie

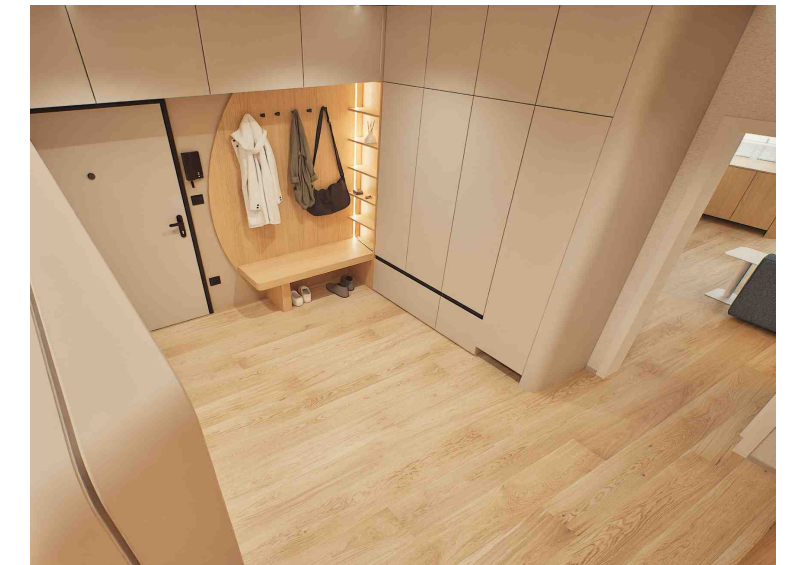
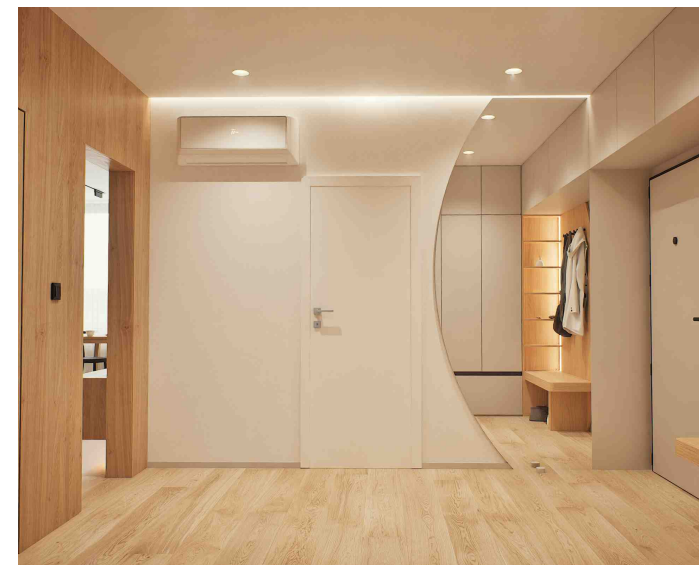
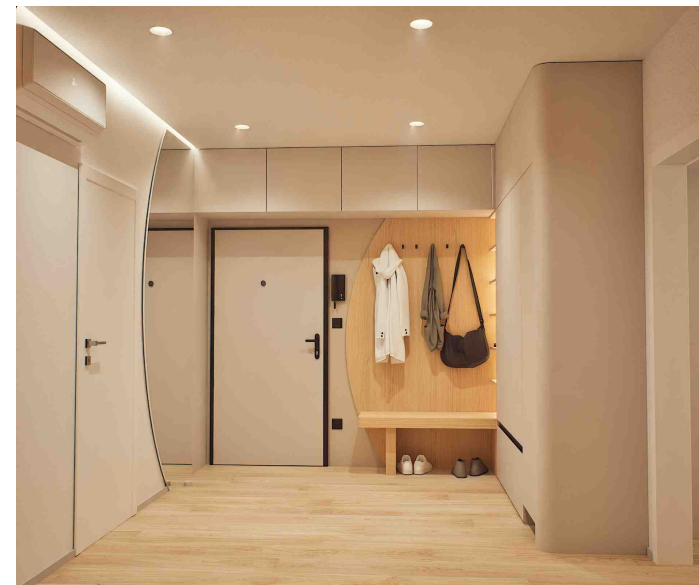


Poznámky

V prípade napájania L1 priamo z rozvodnej skrine vyviezť napájanie priamo v SDK rampe.

Autor: Jakub Pevný	Jednotky	Mierka	Strana
27.07.2026	mm	1:20	5
Elektroinštalácie - 1. Predsieň			

Elektroinštalácie
2. Kúpeľňa

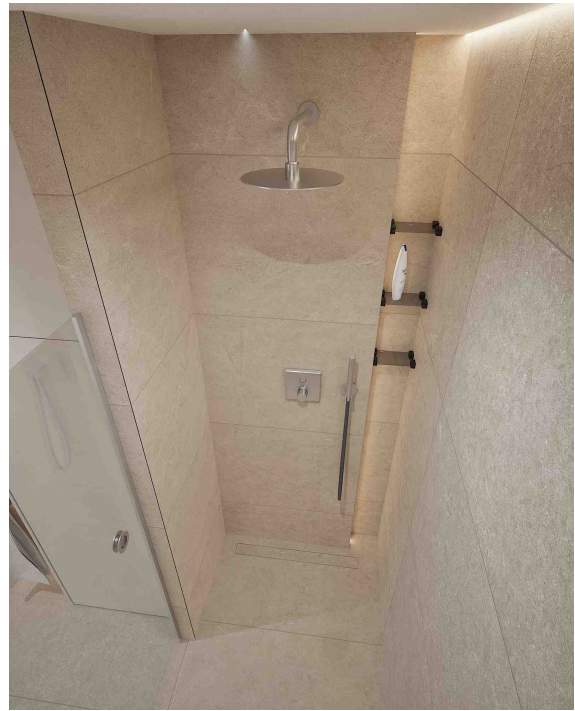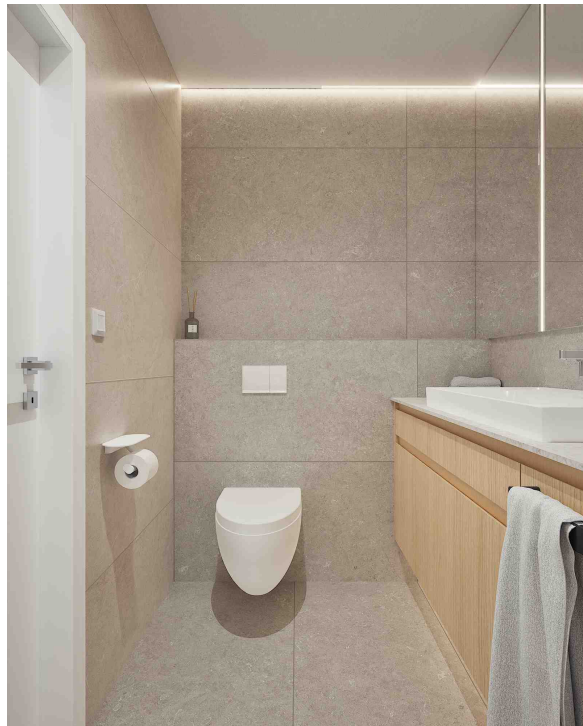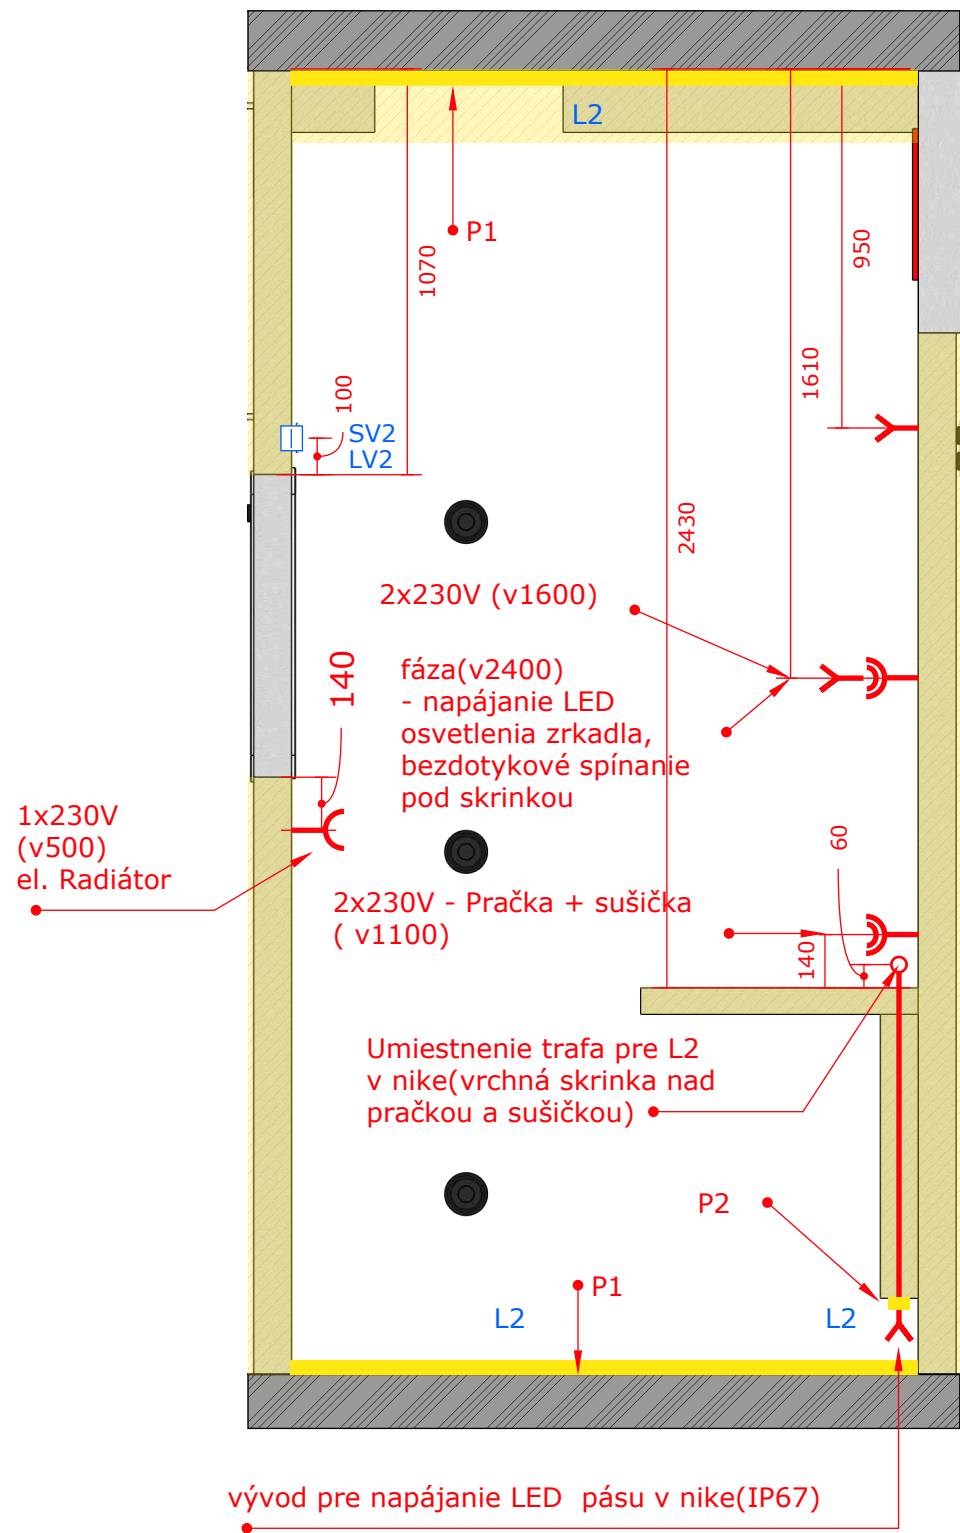

Poznámky


L2 spínané vypínačom (SV/L2) napájanie pre tieto led pásy v skrinke nad pračkou a sušičkou.

P1 - LED Rampa pre nasvietenie obkladov (zo strany SDK prvkov - hĺbka 80mm)

P2 - Vývod napájanie pre L2 v nike pri úrovni stropu z primúrovky.





Autor: Jakub Pevný	Jednotky	Mierka	Strana
27.07.2026	mm	1:20	6
Elektroinštalácie - 2. Kúpeľňa			



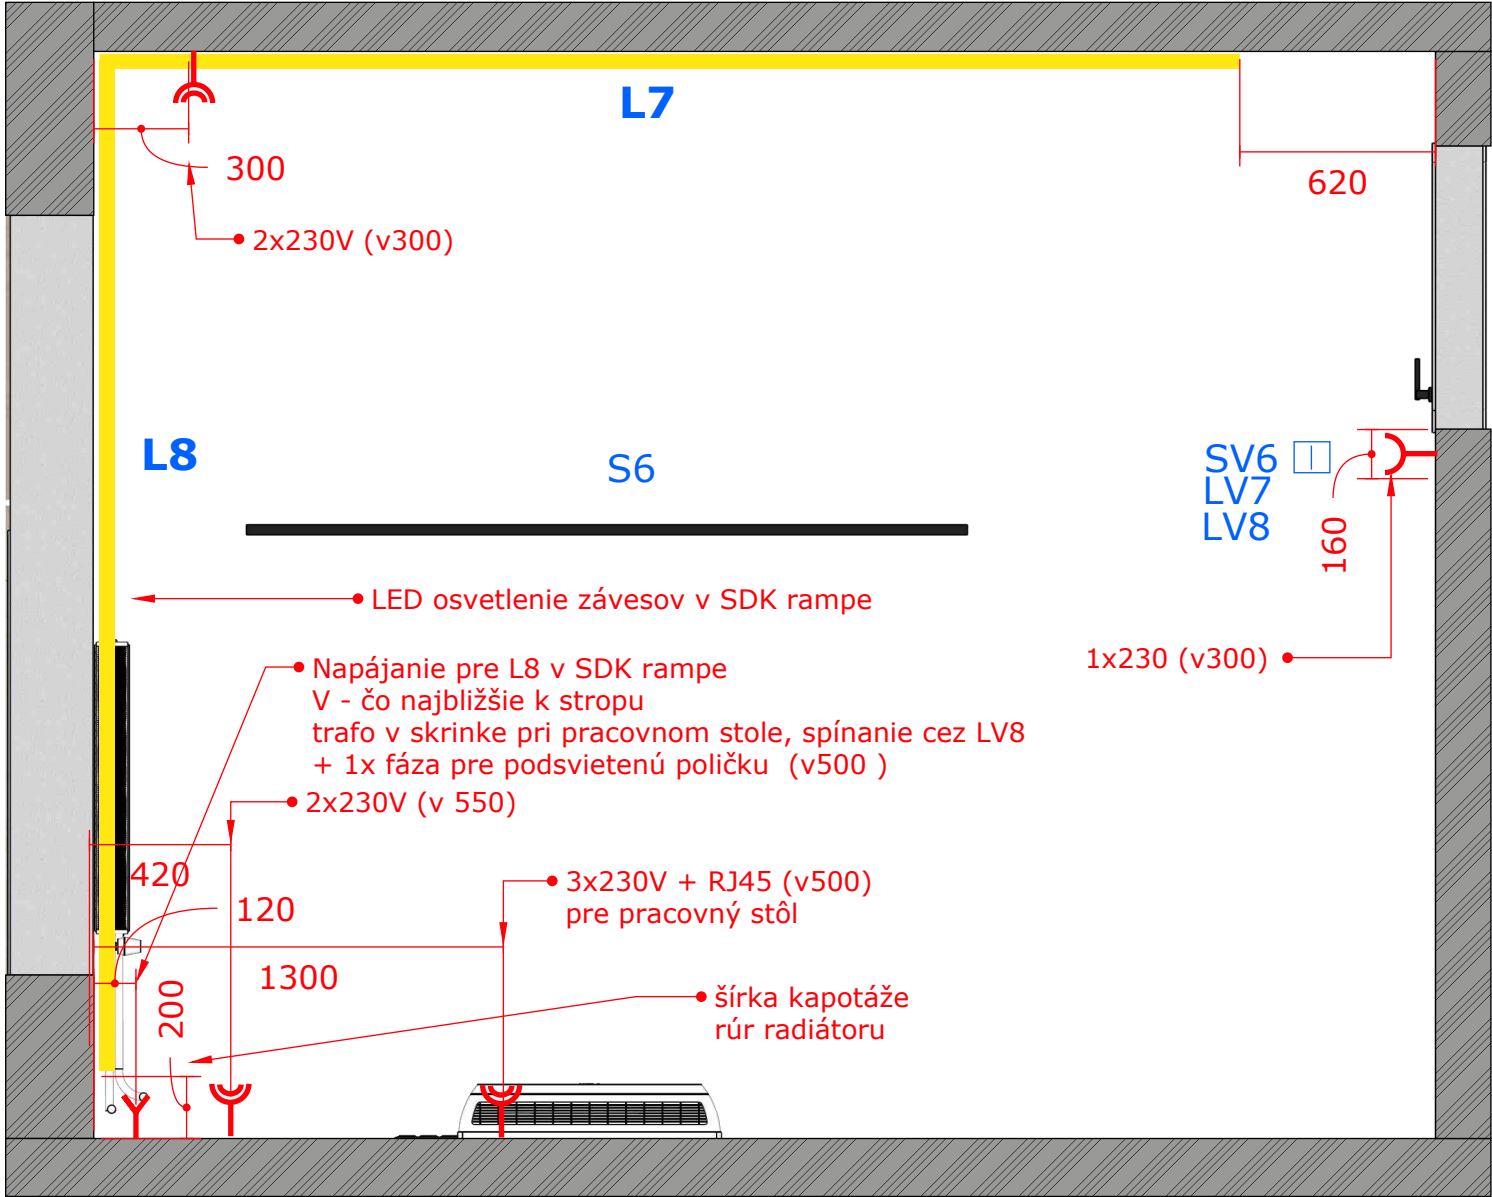


Autor: Jakub Pevný	Jednotky	Mierka	Strana
27.07.2026	mm	1:20	7
Elektroinštalácie - 3. Pracovňa			



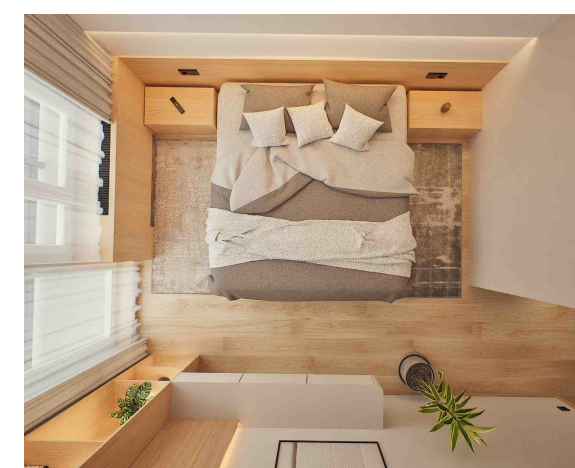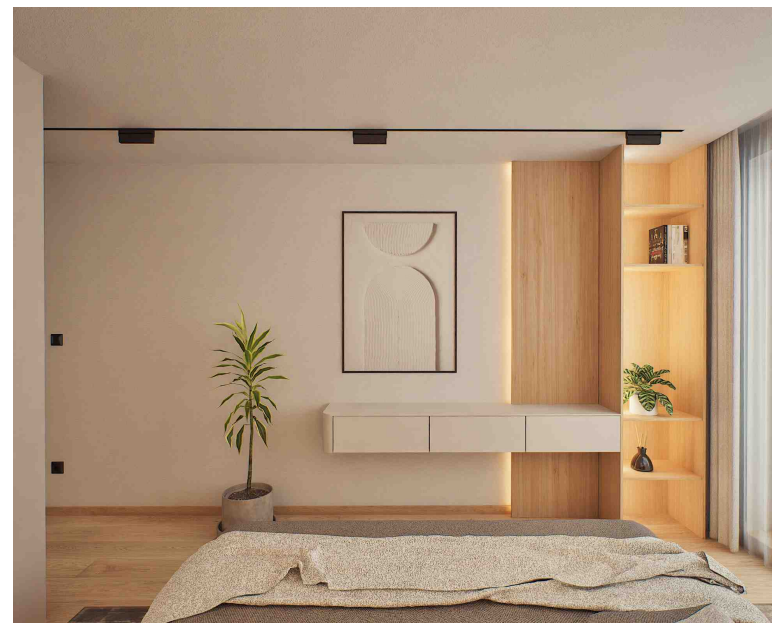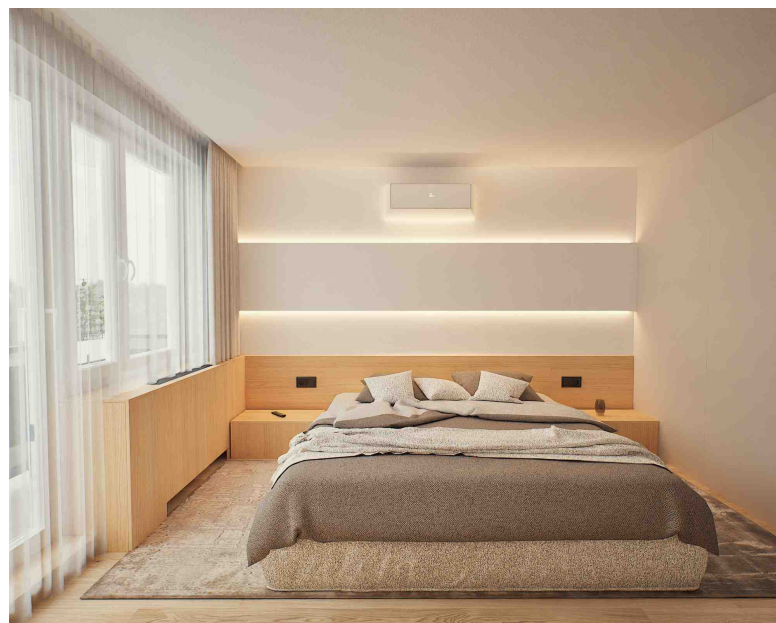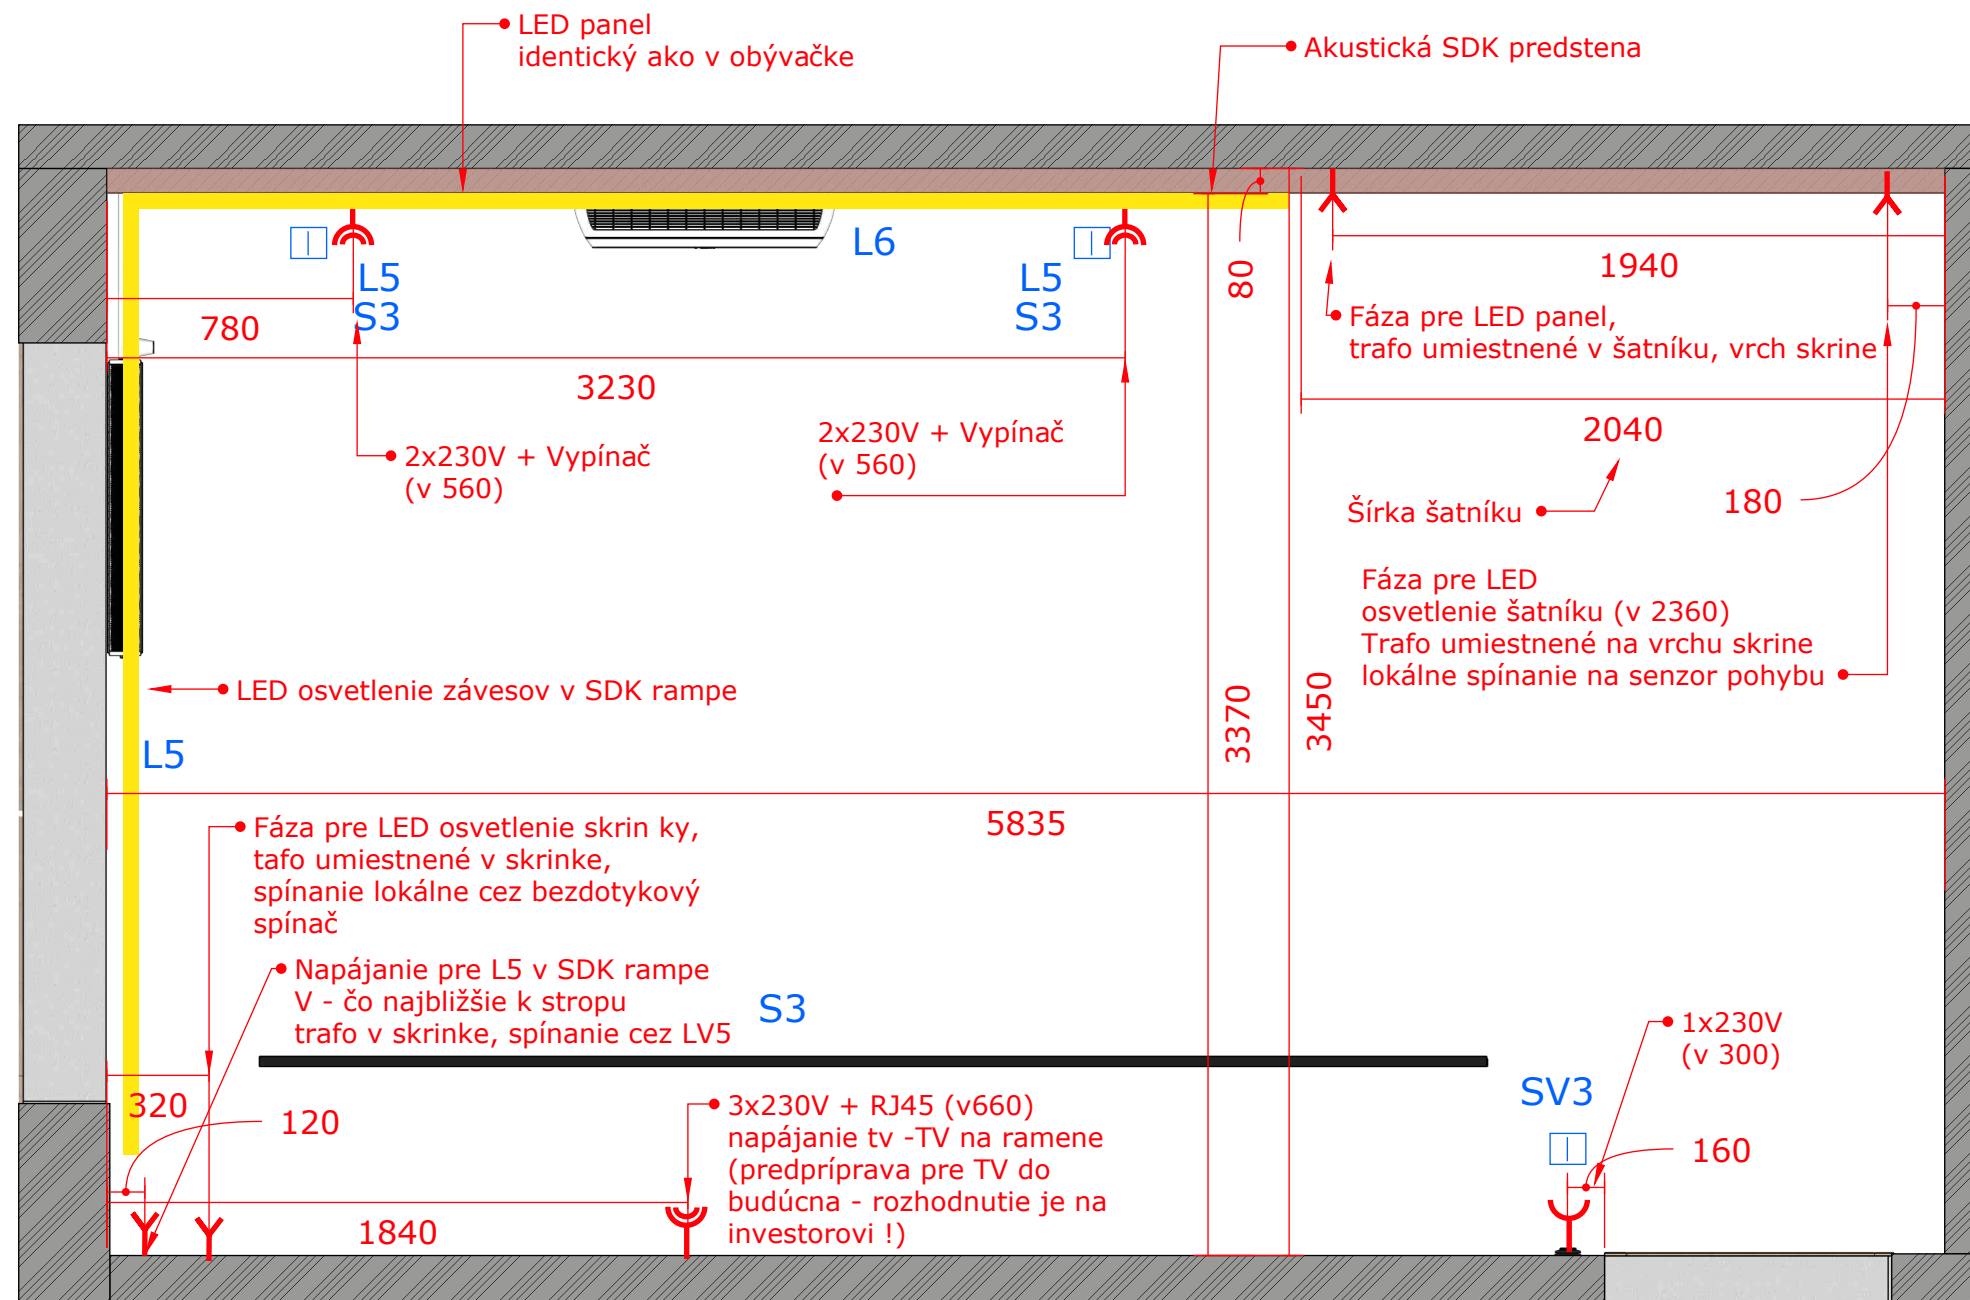



Autor: Jakub Pevný	Jednotky	Mierka	Strana
27.07.2026	mm	1:20	8
Elektroinštalácie - 4. Spálňa			

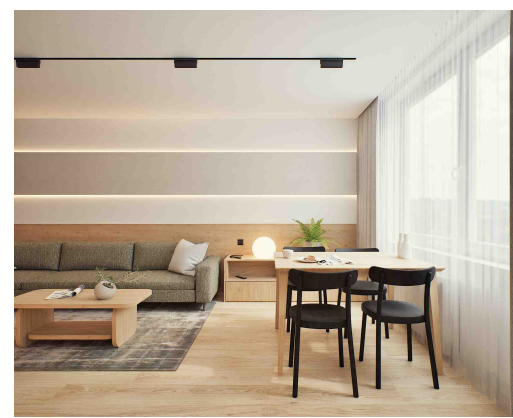

V prípade napájania
z rovodnej skrine vyviezť
káble priamo na ich miesto napájania
k LED


Poznámky

Pri riešení napájania L3,L4,P priamo z
rovodnej skrine vynechať miesta pre trafo.

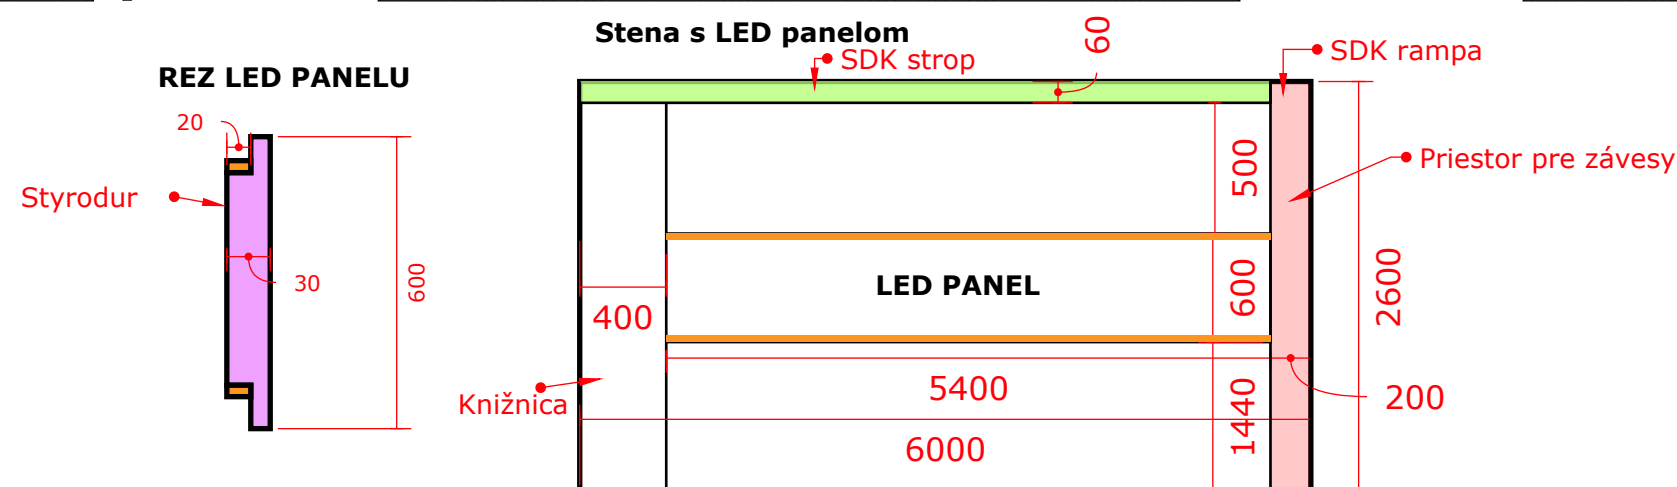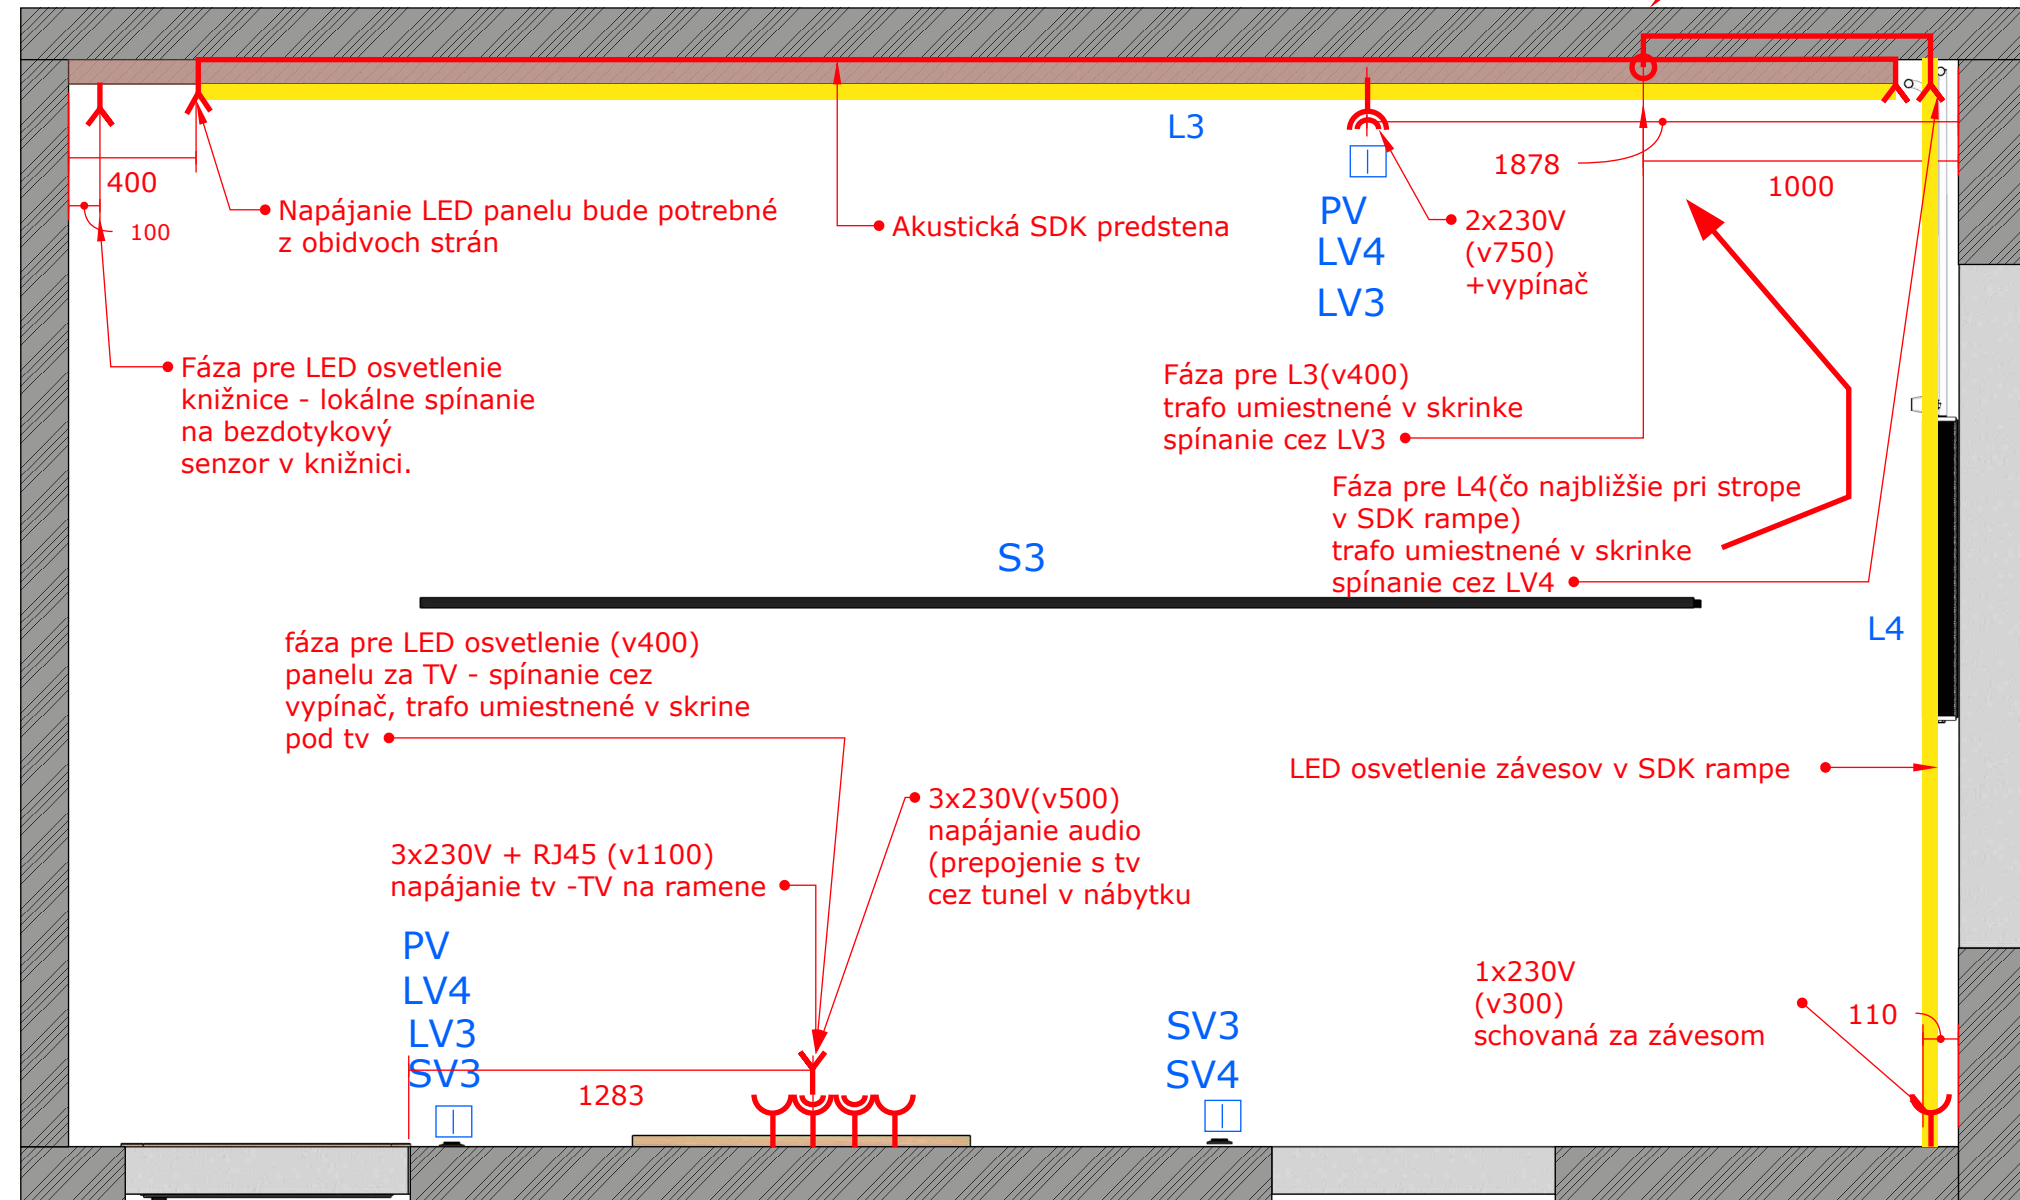


Autor: Jakub Pevný	Jednotky	Mierka	Strana
27.07.2026	mm	1:20	9
Elektroinštalácie - 5. Obývačka			



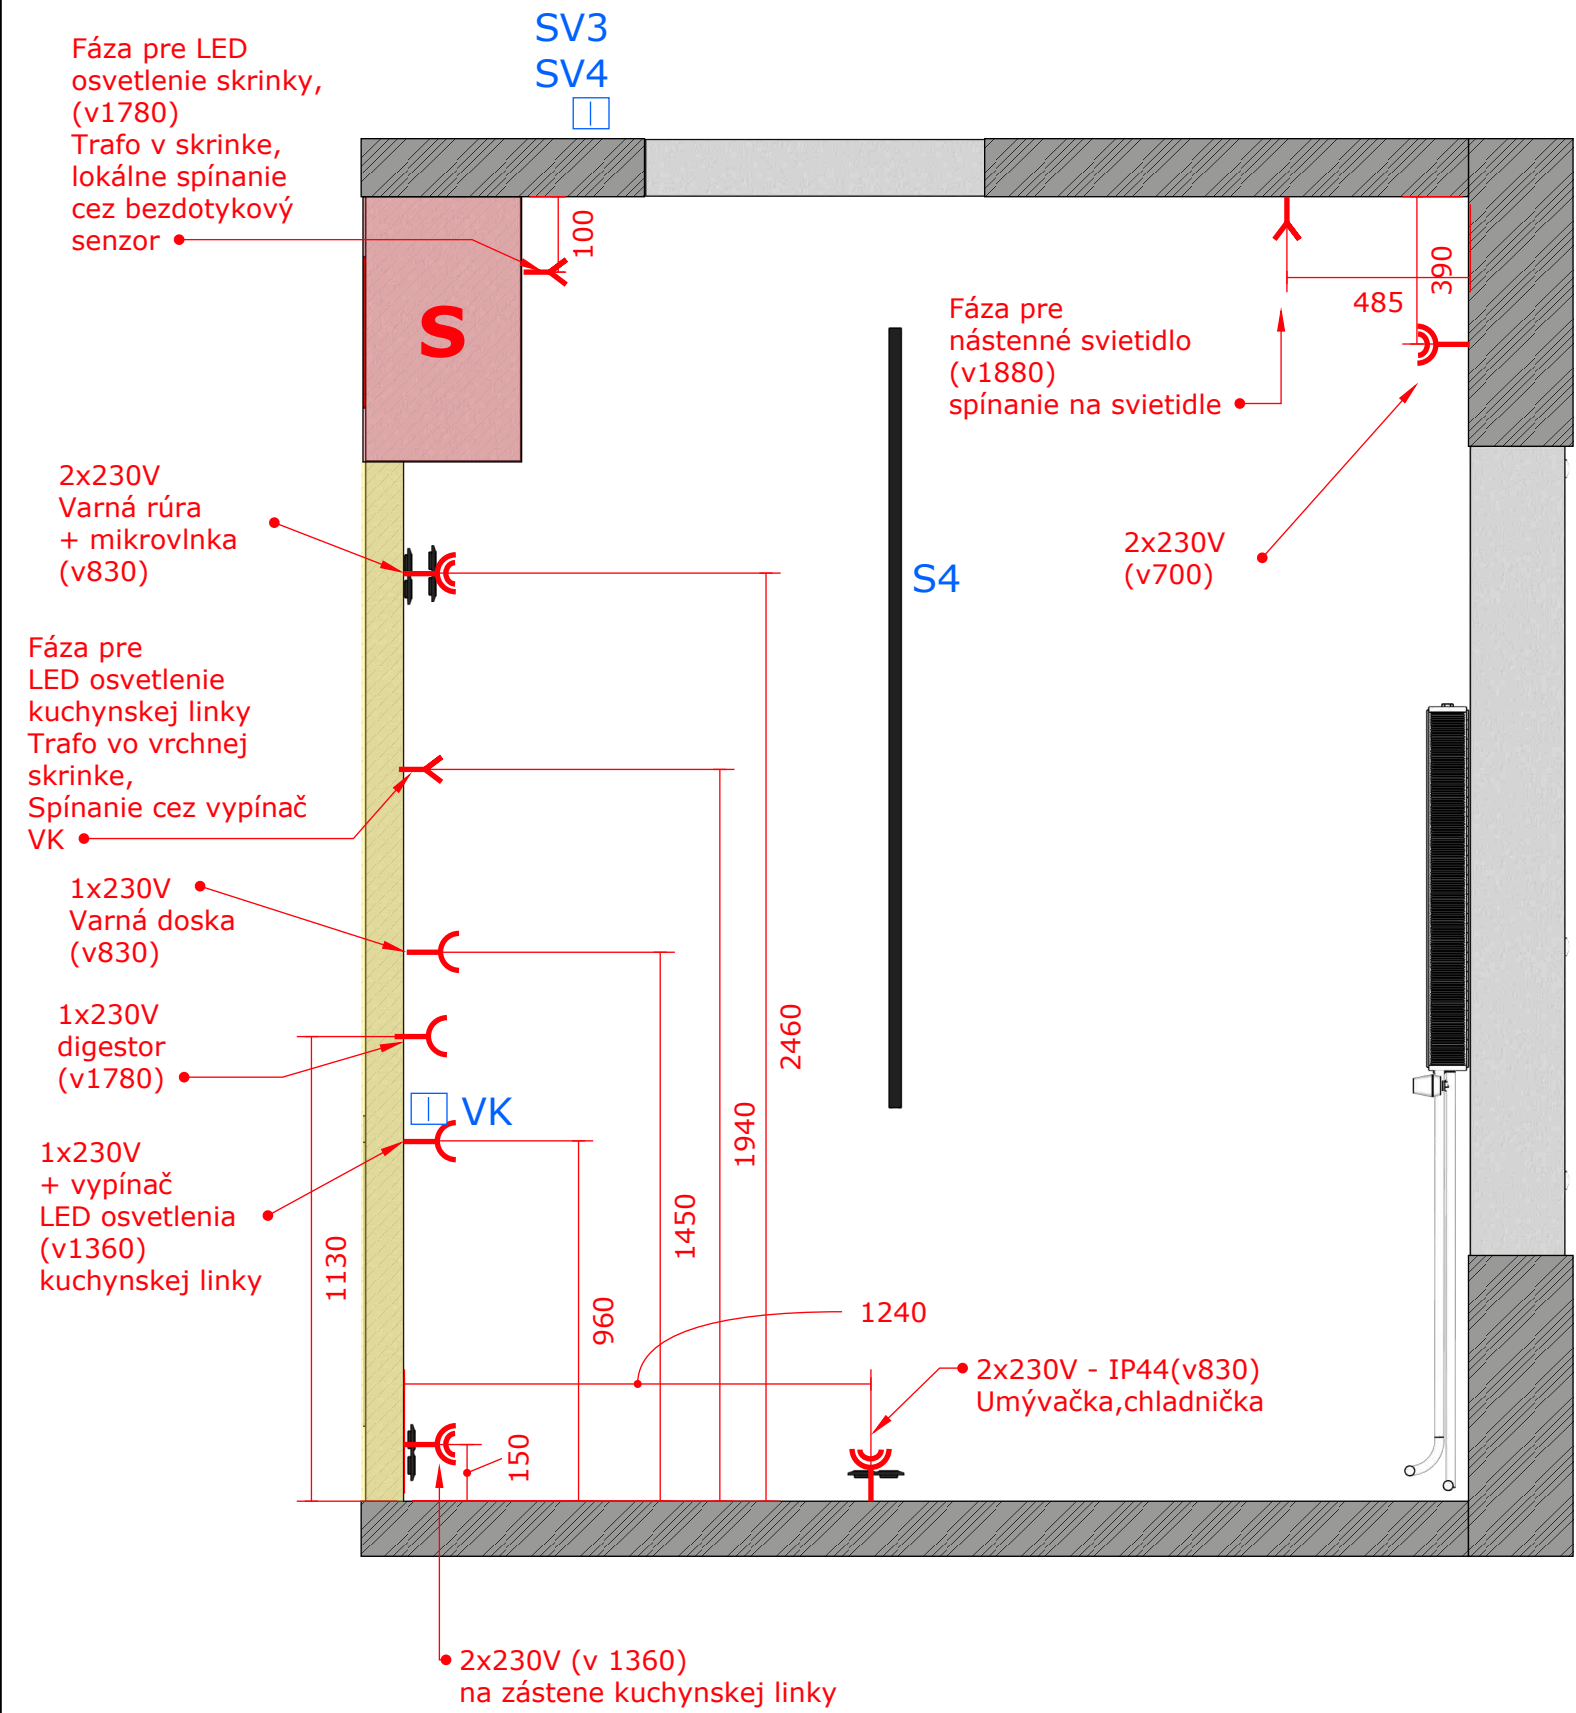

Autor: Jakub Pevný	Jednotky	Mierka	Strana
27.07.2026	mm	1:20	10
Elektroinštalácie - 6. Kuchyňa			




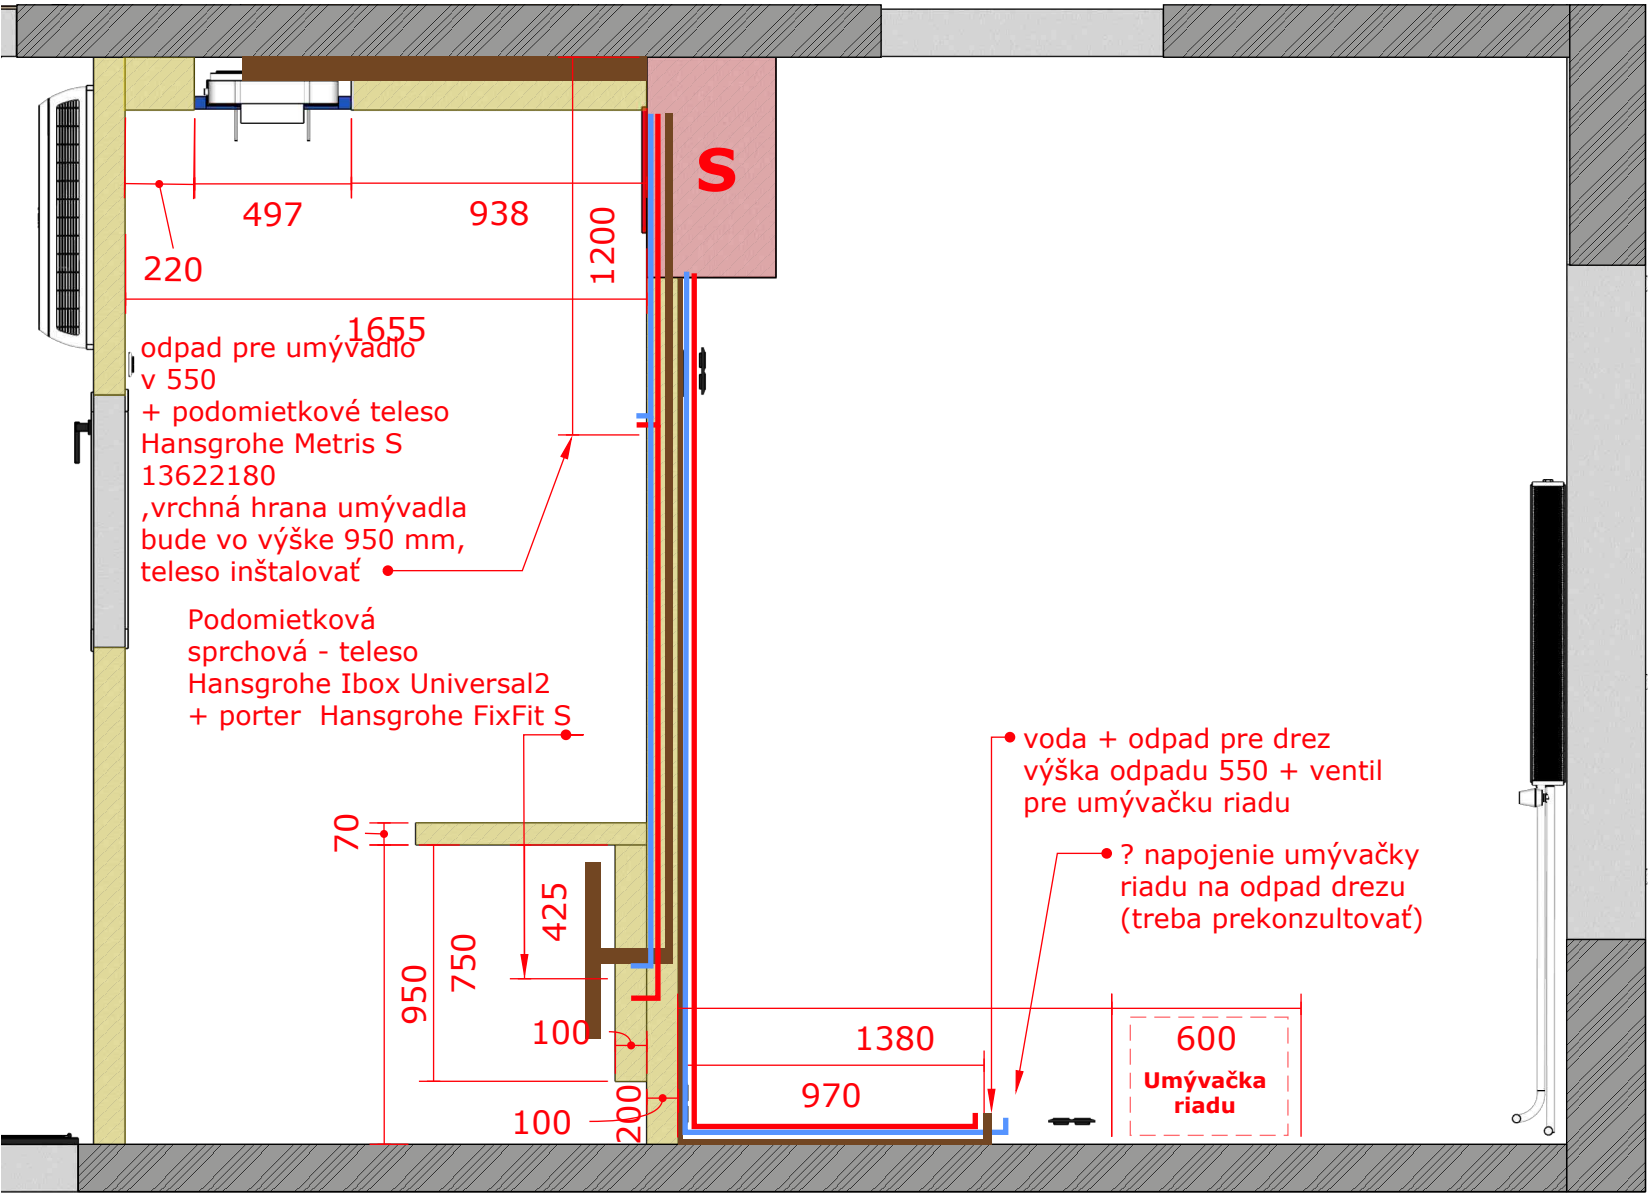

Poznámky

Presná zostava sprchového systému ešte nie je určená.

Inštalačná výška pre podomietkové teleso Metris S

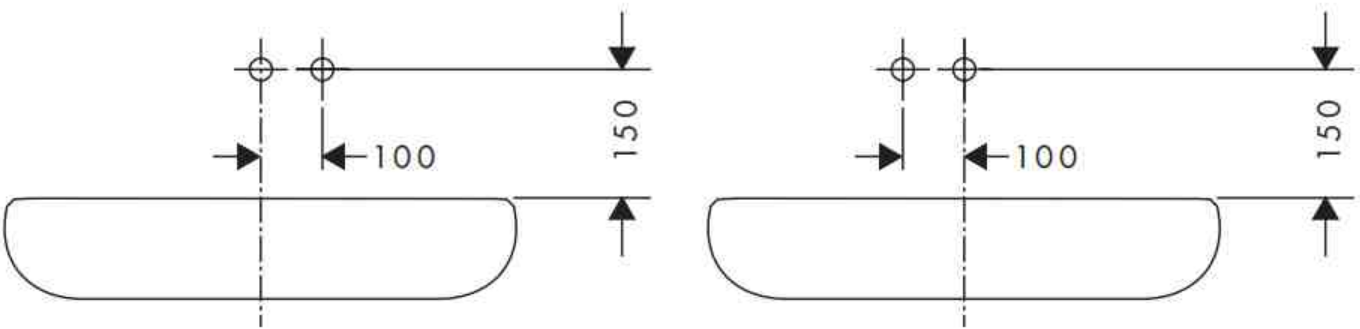

Autor: Jakub Pevný	Jednotky	Mierka	Strana
27.07.2026	mm	1:20	11
ZTI			

